FABRICATION MATERIALS


| PT NO | COMPONENT DESCRIPTION | N.S. (MM) | QTY |
|---|---|---|---|
| | PIPE | | |
| 1 | PIPE SCH10S ASME B36.19 A312Gr.TP304-S | 65 | 360MM |
| | FITTINGS | | |
| 2 | TEE SCH10S BW ASME B16.9 A403Gr.WP304-S | 65 x 65 | 1 |
| 3 | 90DEG LR ELBOW SCH10S BW ASME B16.9 A403Gr.WP304-S | 65 | 1 |
| | FLANGES | | |
| 4 | SLIP-ON FLANGE 150LB RF ASME B16.5 A182Gr.F304 | 65 | 2 |

ERECTION MATERIALS

| PT NO | COMPONENT DESCRIPTION | N.S. (MM) | QTY |
|---|---|---|---|
| | GASKETS | | |
| 5 | SHEET GASKET 150LB RF 1.5t ASME B16.21 Non-Asbestos Sheet | 65 | 2 |
| | VALVES / IN-LINE ITEMS | | |
| 6 | BUTTERFLY VALVE 150LB RF API 609 A351Gr.CF8 | 65 | 2 |

PIPE SPOOLS

SPL2

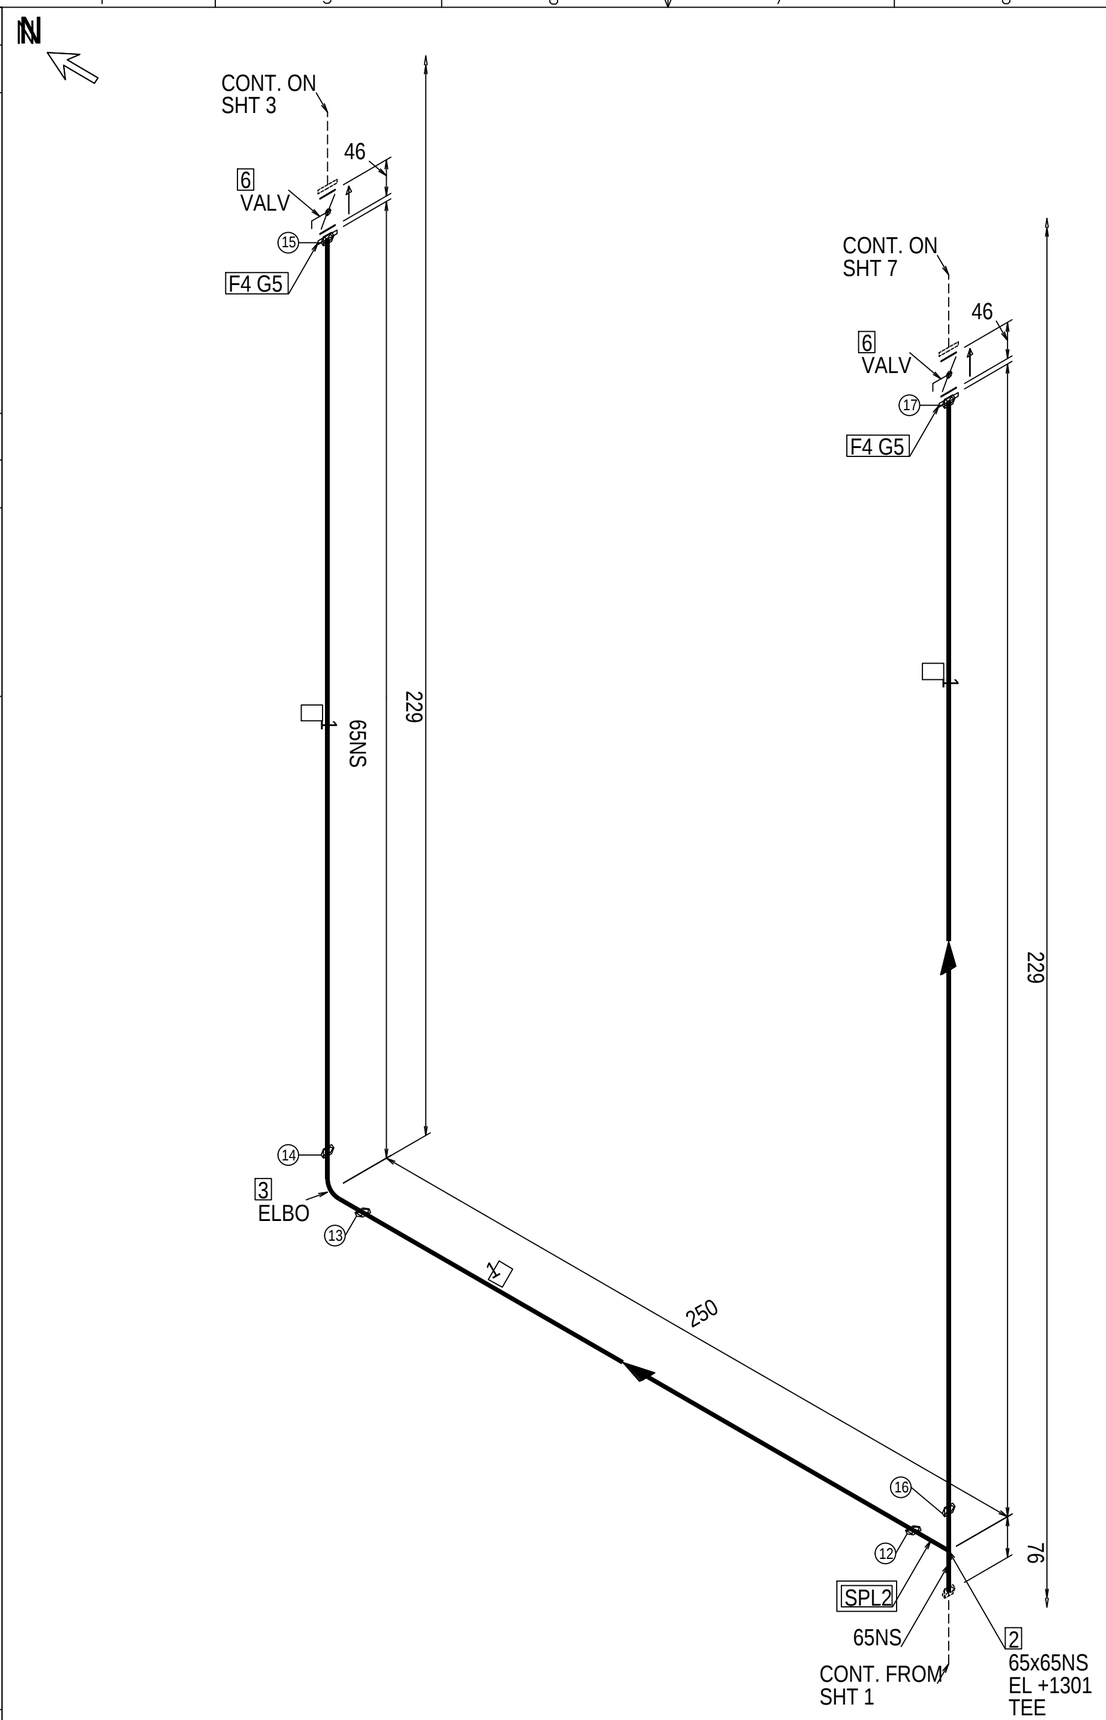


| EN. MANAGER | | |
|---|---|---|
| DESIGN BY | VU DUC HUAN | |
| CHECK BY | | |
| DATE | 2025 | |
| DOCUMENT TITLE: BXLY15T.01_TO_V109_V110_G118 | | ISSUE CODE: FA |
| SHT 2 OF 7 | | REV: A |

SHOP WELD | FIELD WELD | SOCKET WELD | SCREWED JOINT | COMPN JOINT | SITE CONNECTION | PIPE SUPPORT | LAGGED PIPE | TRACED PIPE